MANZANA	LOTE	AREA	PERIMETRO
G	1	120.00	52.00
	2	120.00	52.00
	3	140.00	54.00
	4	140.00	54.00
	5	140.00	54.00
	6	140.00	54.00
	7	140.00	54.00
	8	140.00	54.00
	9	140.00	54.00
	10	140.00	54.00
	11	140.00	54.00
	12	140.00	54.00
	13	140.00	54.00
	14	140.00	54.00
	15	140.00	54.00
	16	140.00	54.00
	17	140.00	54.00
	18	140.00	54.00

MANZANA	LOTE	AREA	PERIMETRO
H	1	158.62	53.98
	2	145.35	53.30
	3	145.35	53.30
	4	145.35	53.30
	5	187.20	74.40
	6	186.60	74.20
	7	186.60	74.20
	8	186.60	74.20
	9	145.35	53.30
	10	145.35	53.30
	11	145.35	53.30
	12	154.87	54.30

MANZANA	LOTE	AREA	PERIMETRO
I	1	535.46	130.55

MANZANA	LOTE	AREA	PERIMETRO
J	1	131.77	51.91
	2	135.68	52.88
	3	146.87	56.36
	4	161.80	60.30
	5	168.80	62.23
	6	146.30	60.77
	7	377.86	90.73

MANZANA	LOTE	AREA	PERIMETRO
K	1	120.00	52.00
	2	120.00	52.00
	3	120.00	52.00
	4	125.69	53.03
	5	150.93	57.54
	6	148.93	56.55
	7	147.90	56.26
	8	146.23	55.69
	9	142.14	54.64
	10	136.42	47.56
	11	125.73	47.11
	12	12.41	17.07
L	1	995.61	153.81

MANZANA	LOTE	AREA	PERIMETRO
M	1	144.22	51.80
	2	142.01	51.53
	3	129.83	48.35
	4	196.44	75.47

MANZANA	LOTE	AREA	PERIMETRO
N	1	159.82	61.16
	2	139.37	53.35
	3	140.00	54.00
	4	140.00	54.00
	5	140.00	54.00
	6	140.00	54.00
	7	140.00	54.00
	8	140.00	54.00
	9	140.00	54.00
	10	140.00	54.00
	11	140.00	54.00
	12	120.00	52.00
	13	120.00	52.00
	14	116.01	47.78
	15	124.90	55.72
	16	157.38	66.54

MANZANA	LOTE	AREA	PERIMETRO
Ñ	1	120.00	52.00
	2	120.00	52.00
	3	120.00	52.00
	4	121.10	51.05
	5	153.96	51.32
	6	145.10	55.44
	7	120.00	52.00
	8	120.00	52.00

MANZANA	LOTE	AREA	PERIMETRO
A	1	132.66	54.49
	2	126.00	54.00
	3	124.01	47.86
	4	121.85	49.84
	5	129.65	53.01
	6	488.49	102.00

MANZANA	LOTE	AREA	PERIMETRO
B	1	152.58	57.85
	2	139.99	54.25
	3	127.40	50.66
	4	125.58	48.26
	5	155.05	50.46
	6	240.45	82.07

MANZANA	LOTE	AREA	PERIMETRO
C	1	147.17	52.41
	2	138.11	51.41
	3	138.11	51.41
	4	138.11	51.41
	5	186.61	74.20
	6	186.61	74.20
	7	186.61	74.20
	8	186.61	74.20
	9	186.61	74.20
	10	186.61	74.20
	11	186.61	74.20
	12	133.04	52.27
	13	124.68	53.78
	14	134.51	57.06
	15	144.33	60.33
	16	163.83	63.73

MANZANA	LOTE	AREA	PERIMETRO
D	1	140.00	54.00
	2	140.00	54.00
	3	140.00	54.00
	4	140.00	54.00
	5	120.00	52.00
	6	120.00	52.00
	7	140.00	54.00
	8	140.00	54.00
	9	140.00	54.00
	10	123.75	56.00
	11	151.78	58.49
	12	148.22	56.60
	13	153.01	54.55
	14	127.59	49.30
	15	147.52	53.17
	16	152.49	51.45
	17	152.29	52.40
	18	140.00	54.00
	19	140.00	54.00
	20	140.00	54.00

MANZANA	LOTE	AREA	PERIMETRO
E	1	127.24	54.63
	2	136.03	53.12
	3	122.65	49.30
	4	166.49	67.72
	5	170.43	66.72
	6	172.70	67.83
	7	168.00	68.00
	8	140.00	54.00
	9	140.00	54.00
	10	140.00	54.00
	11	140.00	54.00
	12	120.00	52.00
	13	120.00	52.00

MANZANA	LOTE	AREA	PERIMETRO
F	1	120.00	52.00
	2	140.00	54.00
	3	140.00	54.00
	4	140.00	54.00
	5	140.00	54.00
	6	140.00	54.00
	7	140.00	54.00
	8	140.00	54.00
	9	140.00	54.00
	10	140.00	54.00
	11	140.00	54.00
	12	140.00	54.00
	13	140.00	54.00
	14	140.00	54.00
	15	659.90	141.32

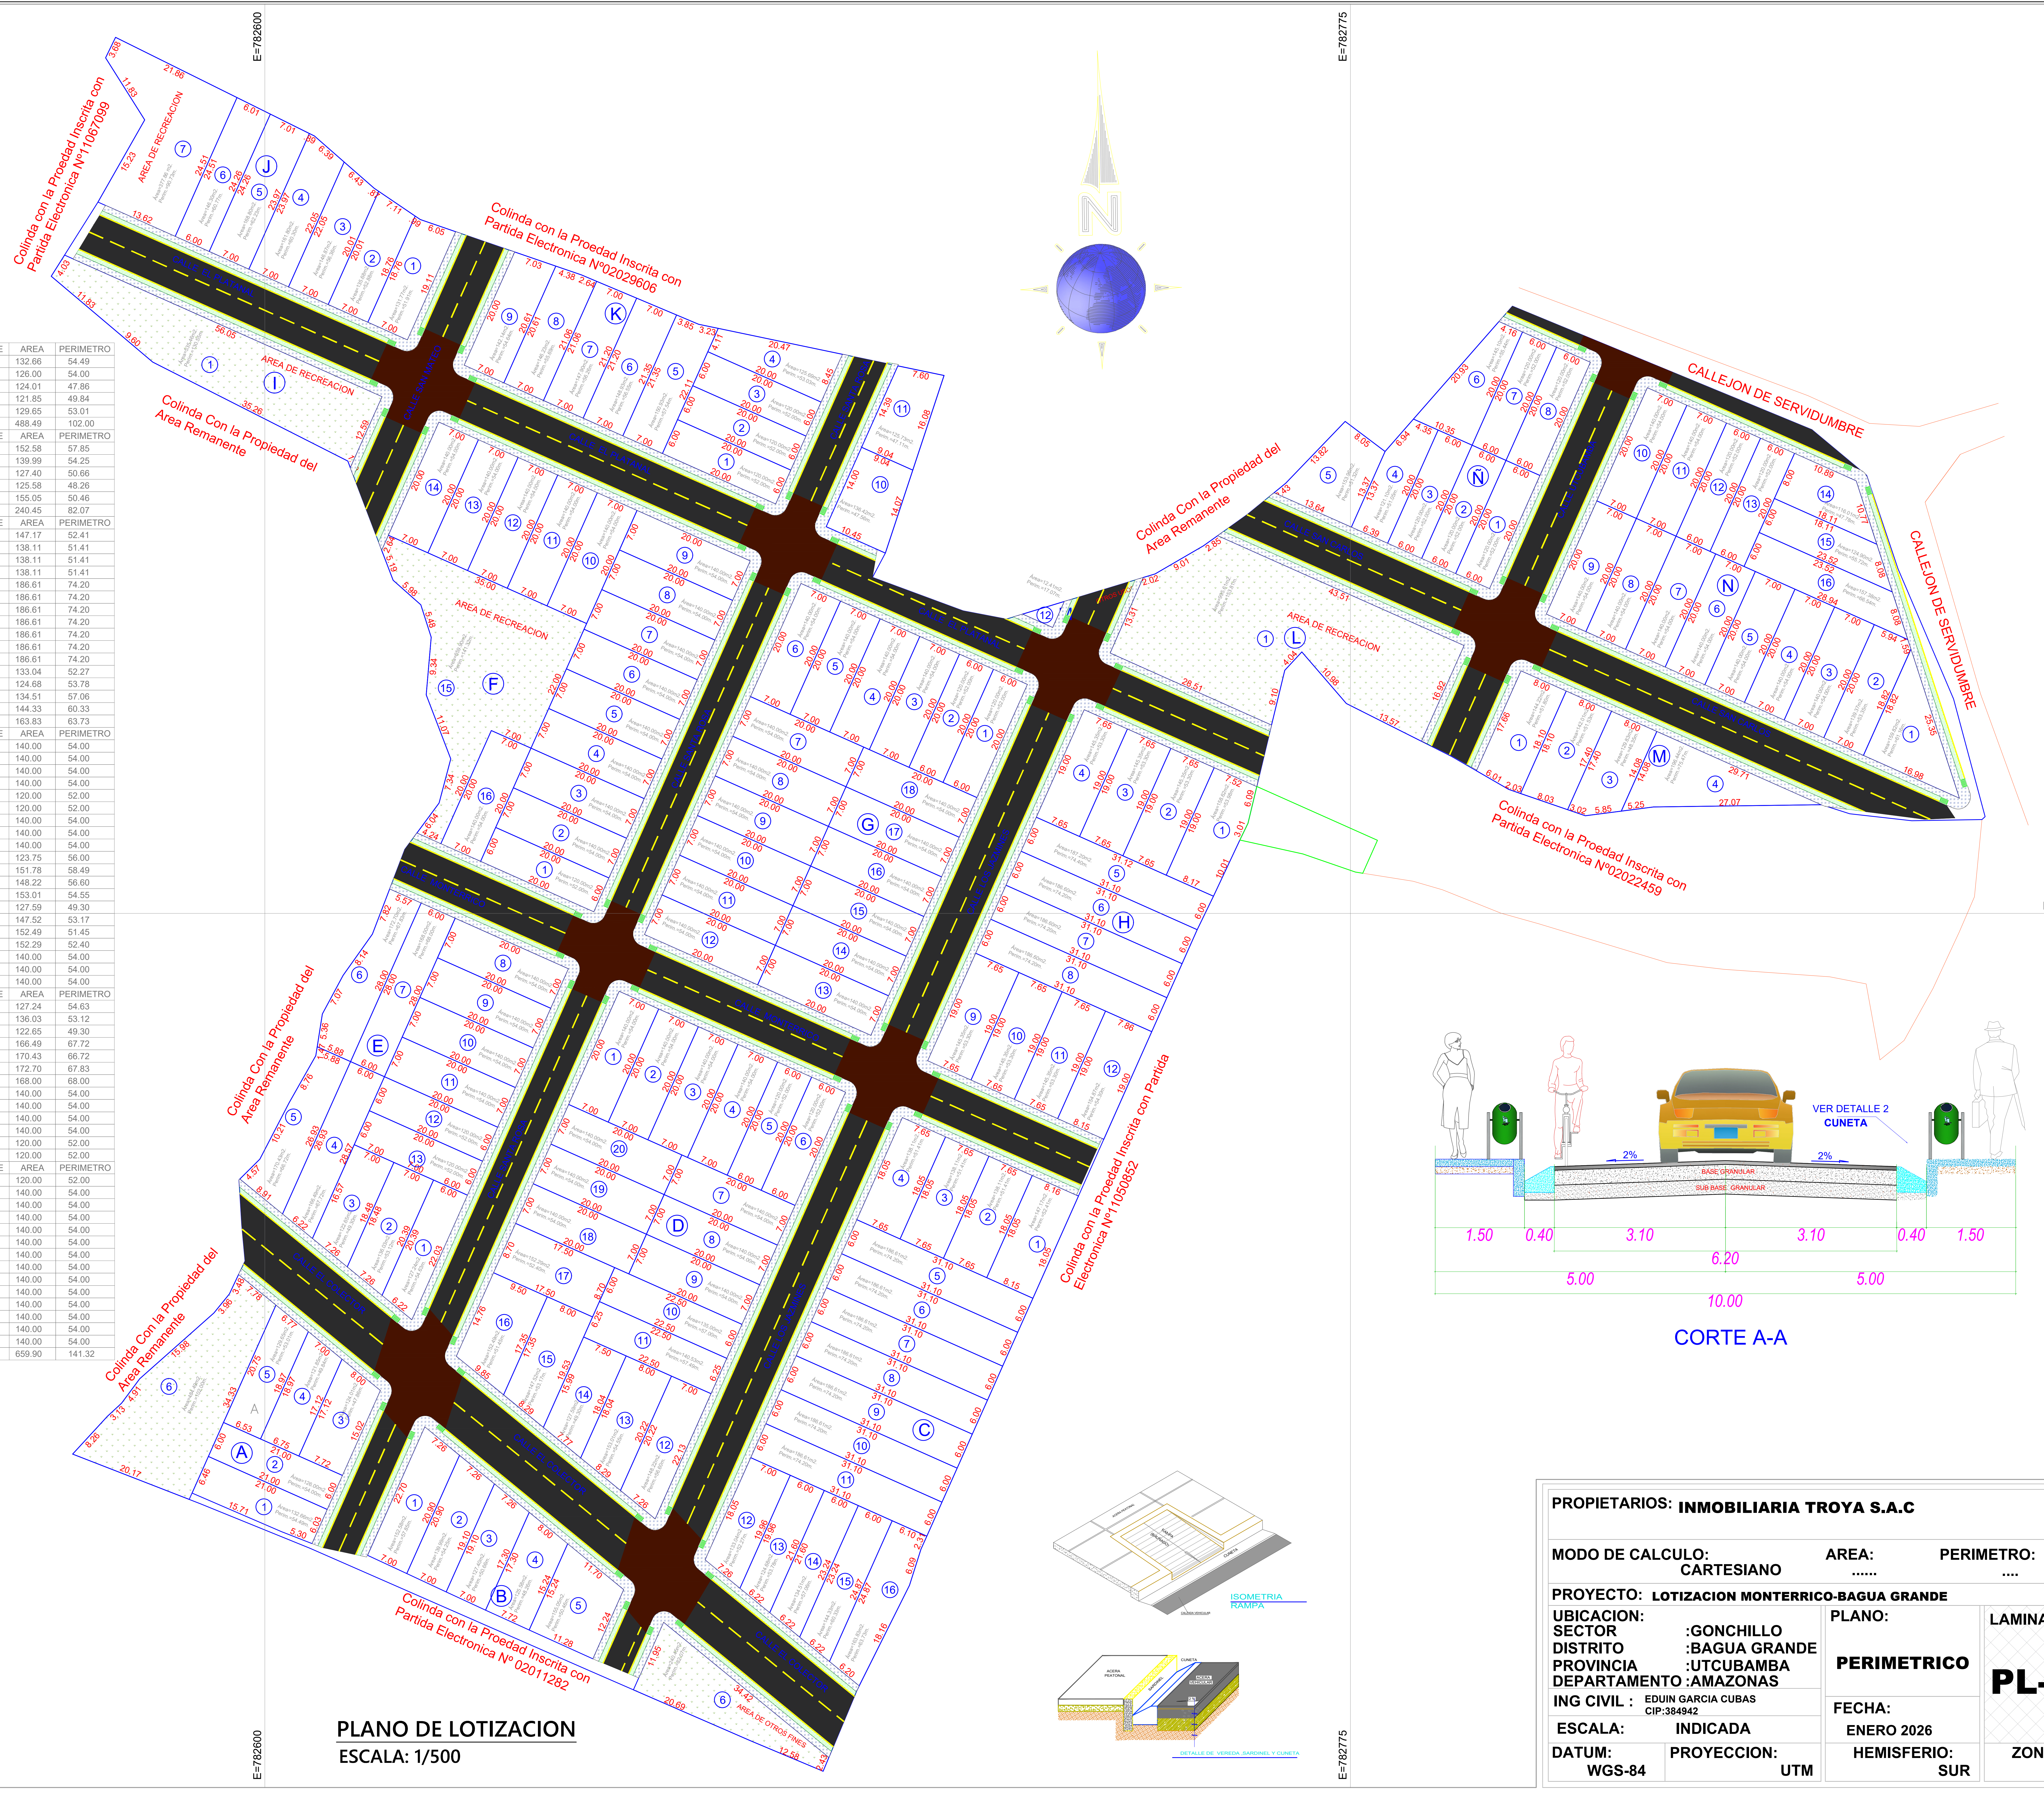
E=782600
E=782775
N=9364600
N
Colinda con la Proedad Inscrita con Partida Electronica N°11067099
Colinda con la Proedad Inscrita con Partida Electronica N°02029606
Colinda Con la Propiedad del Area Remanente
AREA DE RECREACION
CALLEJON DE SERVIDUMBRE
CALLEJON DE SERVIDUMBRE
Colinda Con la Propiedad del Area Remanente
Colinda con la Proedad Inscrita con Partida Electronica N°02022459
Colinda Con la Propiedad del Area Remanente
Colinda con la Proedad Inscrita con Partida Electronica N°11050852
Colinda Con la Propiedad del Area Remanente
Colinda con la Proedad Inscrita con Partida Electronica N° 02011282
AREA DE OTROS FINES
A
B
C
D
E
F
G
H
I
J
K
L
M
N
Ñ
VER DETALLE 2
CUNETA
2%
2%
BASE GRANULAR
SUB BASE GRANULAR
1.50
0.40
3.10
3.10
0.40
1.50
6.20
5.00
5.00
10.00
ACERA PEATONAL
RAMPA (BRUÑADO)
CUNETA
CALZADA VEHICULAR
ACERA PEATONAL
SARDINEL
CUNETA
ACERA VEHICULAR
2 %

CORTE A-A

ISOMETRIA RAMPA

DETALLE DE VEREDA ,SARDINEL Y CUNETA

PLANO DE LOTIZACION

ESCALA: 1/500

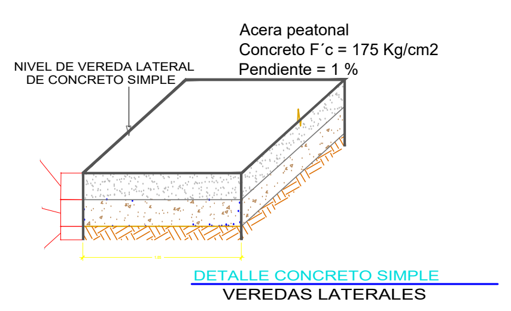
Acera peatonal
Concreto F´c = 175 Kg/cm2
Pendiente = 1 %
NIVEL DE VEREDA LATERAL DE CONCRETO SIMPLE

DETALLE CONCRETO SIMPLE
VEREDAS LATERALES

PROPIETARIOS: **INMOBILIARIA TROYA S.A.C**

MODO DE CALCULO: CARTESIANO
AREA: ......
PERIMETRO: ....

PROYECTO: **LOTIZACION MONTERRICO-BAGUA GRANDE**

UBICACION:
SECTOR :GONCHILLO
DISTRITO :BAGUA GRANDE
PROVINCIA :UTCUBAMBA
DEPARTAMENTO :AMAZONAS

ING CIVIL : EDUIN GARCIA CUBAS
CIP:384942

ESCALA: INDICADA

PLANO: **PERIMETRICO**

FECHA: ENERO 2026

LAMINA N°: **PL-01**

DATUM: WGS-84
PROYECCION: UTM
HEMISFERIO: SUR
ZONA: 17